


PROYECTO GEOCAV LTDA.	CONTENIDO SONDAJE ROTACION N° 1	ESCALA SIN ESCALA
LABORATORIO SUELOTEC LTDA.	UBICACION LOTE Y2 AVENIDA CARDENAL JORGE MEDINA E COQUIMBO - IV REGION	FECHA JULIO 2017
		ARCHIVO: ESTRATIGRAFIA SLOTE Y2

**SONDAJE
ROTACION N° 1**

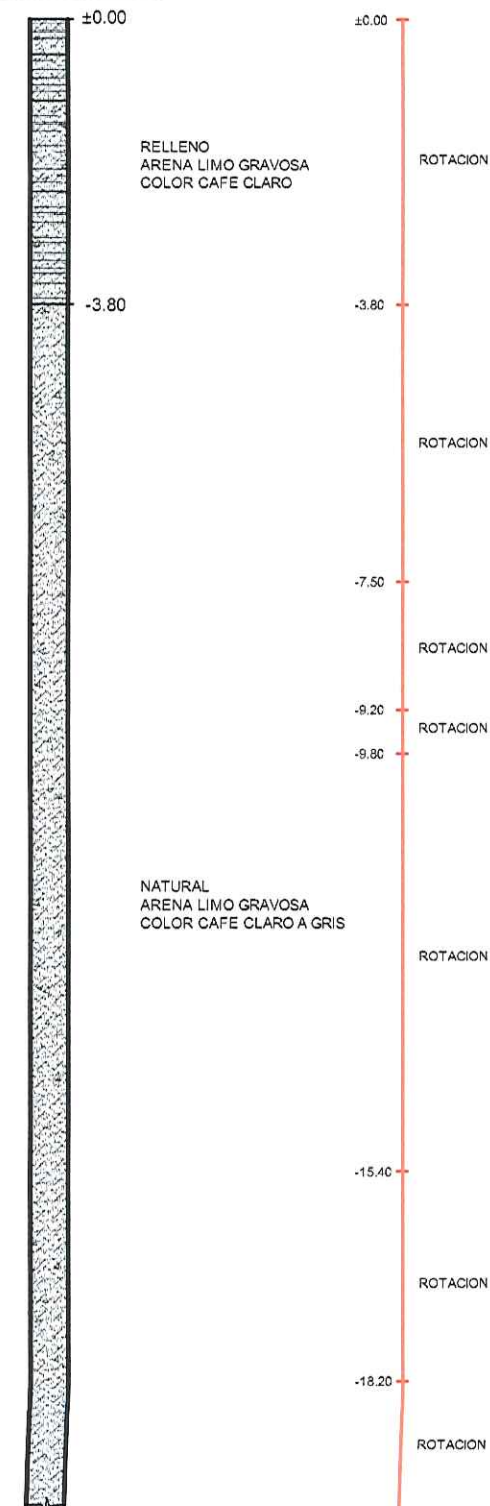

CONTINUA

CONTINUACION

